


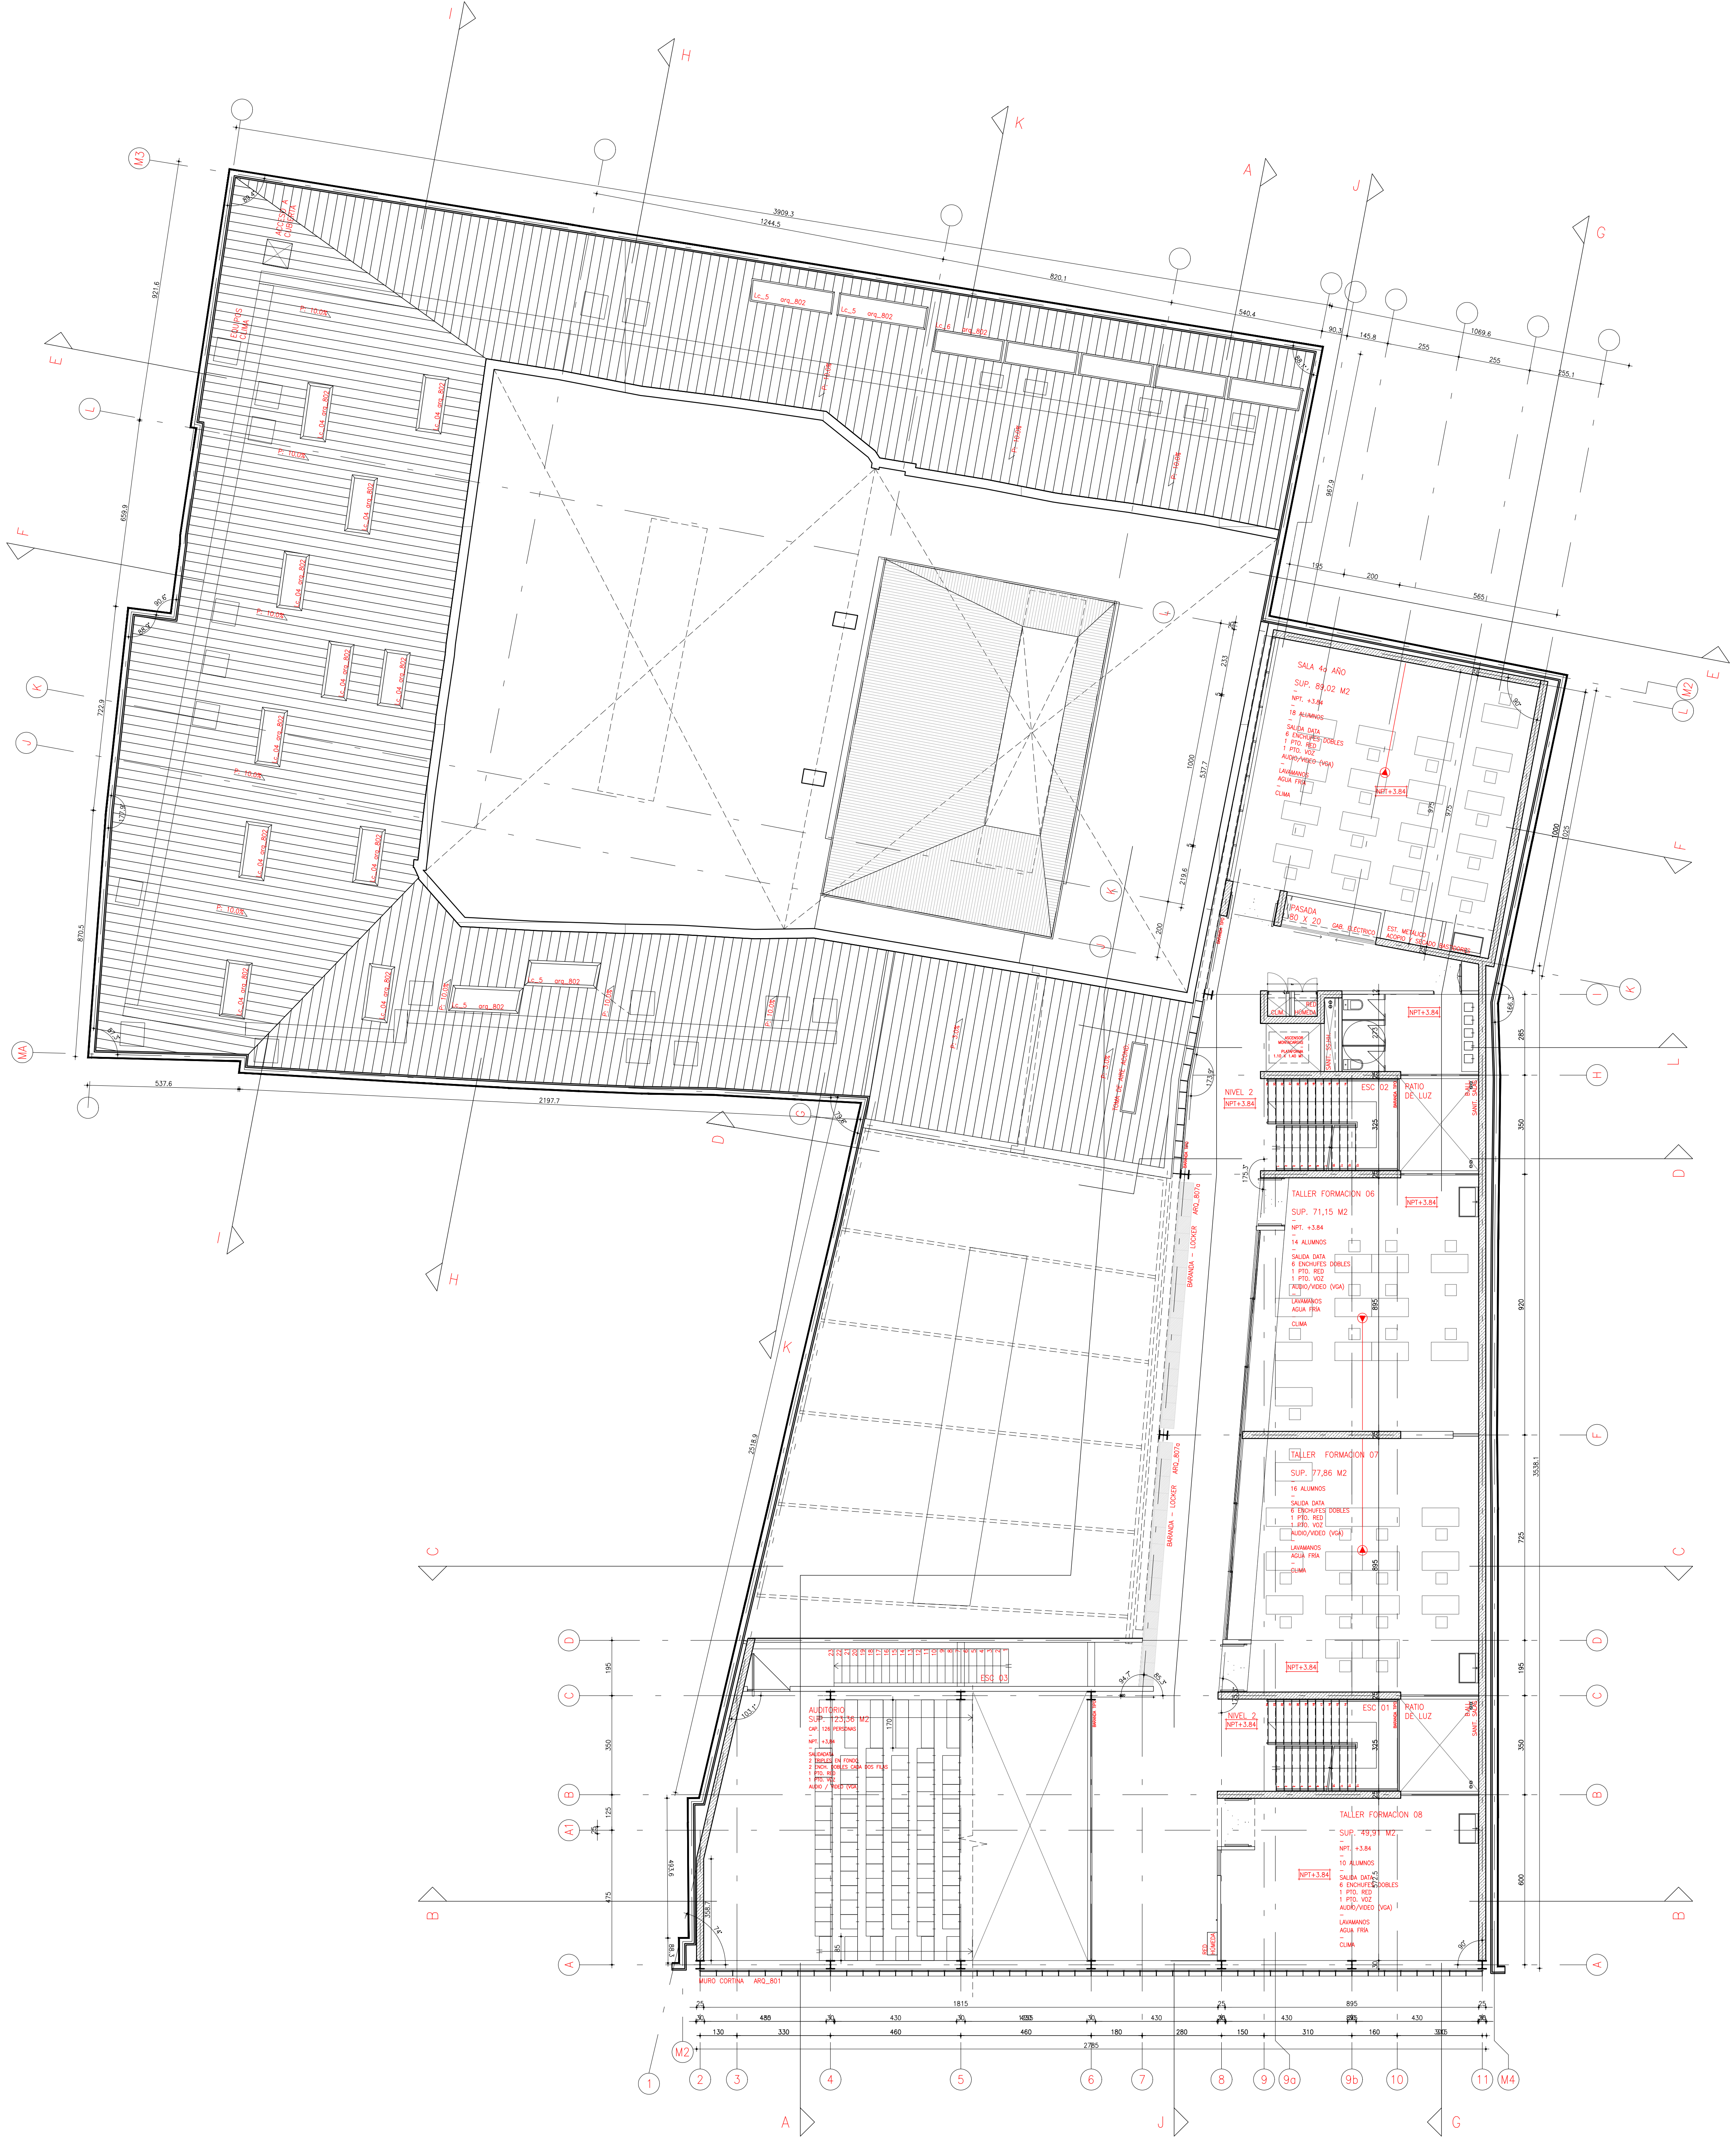

ESPECIALISTAS

COORDINADOR GENERAL
RESPECTA S.A.
RUT: 15.110.880-0
TEL: 56-2-22222222
E-MAIL: info@respecta.cl

INGENIERIA DE CLIMATIZACION
RAUL PAEZ INGENIERIA
RUT: 15.110.880-0
TEL: 56-2-22222222
E-MAIL: info@raulpaez.cl

INGENIERIA ELECTRICA
T & P
RUT: 15.110.880-0
TEL: 56-2-22222222
E-MAIL: info@tamp.cl

CALCULO ESTRUCTURAL
MARIO RODRIGUEZ LUNA
RUT: 15.110.880-0
TEL: 56-2-22222222
E-MAIL: info@marioRodriguez.cl

INGENIERIA SANITARIA
JULIO B. VILLALBA
RUT: 15.110.880-0
TEL: 56-2-22222222
E-MAIL: info@julioB.cl

ILUMINACION
DIP
RUT: 15.110.880-0
TEL: 56-2-22222222
E-MAIL: info@dip.cl

SEGURIDAD CONTRA INCENDIOS
IX
RUT: 15.110.880-0
TEL: 56-2-22222222
E-MAIL: info@ix.cl

SEGURIDAD
DIRECCION
RUT: 15.110.880-0
TEL: 56-2-22222222
E-MAIL: info@seguridad.cl

ABSLACION ACUSTICA
DIRECCION
RUT: 15.110.880-0
TEL: 56-2-22222222
E-MAIL: info@absolucion.cl

AUDIO Y VIDEO
DIRECCION
RUT: 15.110.880-0
TEL: 56-2-22222222
E-MAIL: info@audioyvideo.cl

APTO PARA CONSTRUCCION

OFArquitectos
+ Miguel Cassassus

OP	MODIFICACIONES	UB	VVP	FECHA

VERSION	FECHA	APROBACION PROYECTUAL

ARQUITECTURA

ARQUITECTURA
A R Q U I T E C T O S
MIGUEL CASSASSUS
FERNANDO GERRERA
ALVARO RAMIREZ

COLABORADORES

EL CACIQUE 6983 - OF. A
PROVIDENCIA - SANTIAGO
FONO: 56-2- 8033248
EMAIL: info@elcacique.cl

M A N D A N T E
UNIVERSIDAD DIEGO PORTALES
FONO: 67000000

REPRESENTANTE LEGAL

DIRECTOR DE ADMINISTRACION
E INFRAESTRUCTURA
RODRIGO VELAZ

UBICACION
SALVADOR SANFuentes 2221
SANTIAGO - SANTIAGO

NORTE

PROYECTO: FACULTAD DE
ARQUITECTURA ARTE Y DISEÑO
UNIVERSIDAD DIEGO PORTALES

CONTENIDO: PLANTA 2DO NIVEL

DETALLE	FECHA	FECHA

ESCALA	FECHA	FECHA

PLANO N°	FECHA	FECHA

PROYECTO: FACULTAD DE ARQUITECTURA ARTE Y DISEÑO